AREA STATEMENT

PLOT NOS.	AREA SQ.YD.	PLOT NOS.	A SC
PLOT 1	230.00	PLOT 194 TO 199	50.0
PLOT 2	179.50	PLOT 200 TO 203	58.33
PLOT 3	195.00	PLOT 204 TO 261	50.00
PLOT 4	201.00	PLOT 262 TO 299	100.00
PLOT 5	182.50	PLOT 300	208.00
PLOT 6	185.00	PLOT 301 TO 315	100.00
PLOT 7	189.80	PLOT 316	96.50
PLOT 8 TO 91	100.00	PLOT 317	84.50
PLOT 92	58.33	PLOT 318	72.00
PLOT 93	58.33	PLOT 319	61.50
PLOT 94 TO 122	50.00	PLOT 320	65.50
PLOT 123 TO 126	58.33	PLOT 321 TO 345	100.00
PLOT 127 TO 156	50.00	PLOT 346	179.00
PLOT 157 TO 160	58.33	PLOT 347 TO 391	100.00
PLOT 162 TO 189	50.00	PLOT 392	154.50
PLOT 190 TO 193	58.33	PLOT 393	193.00

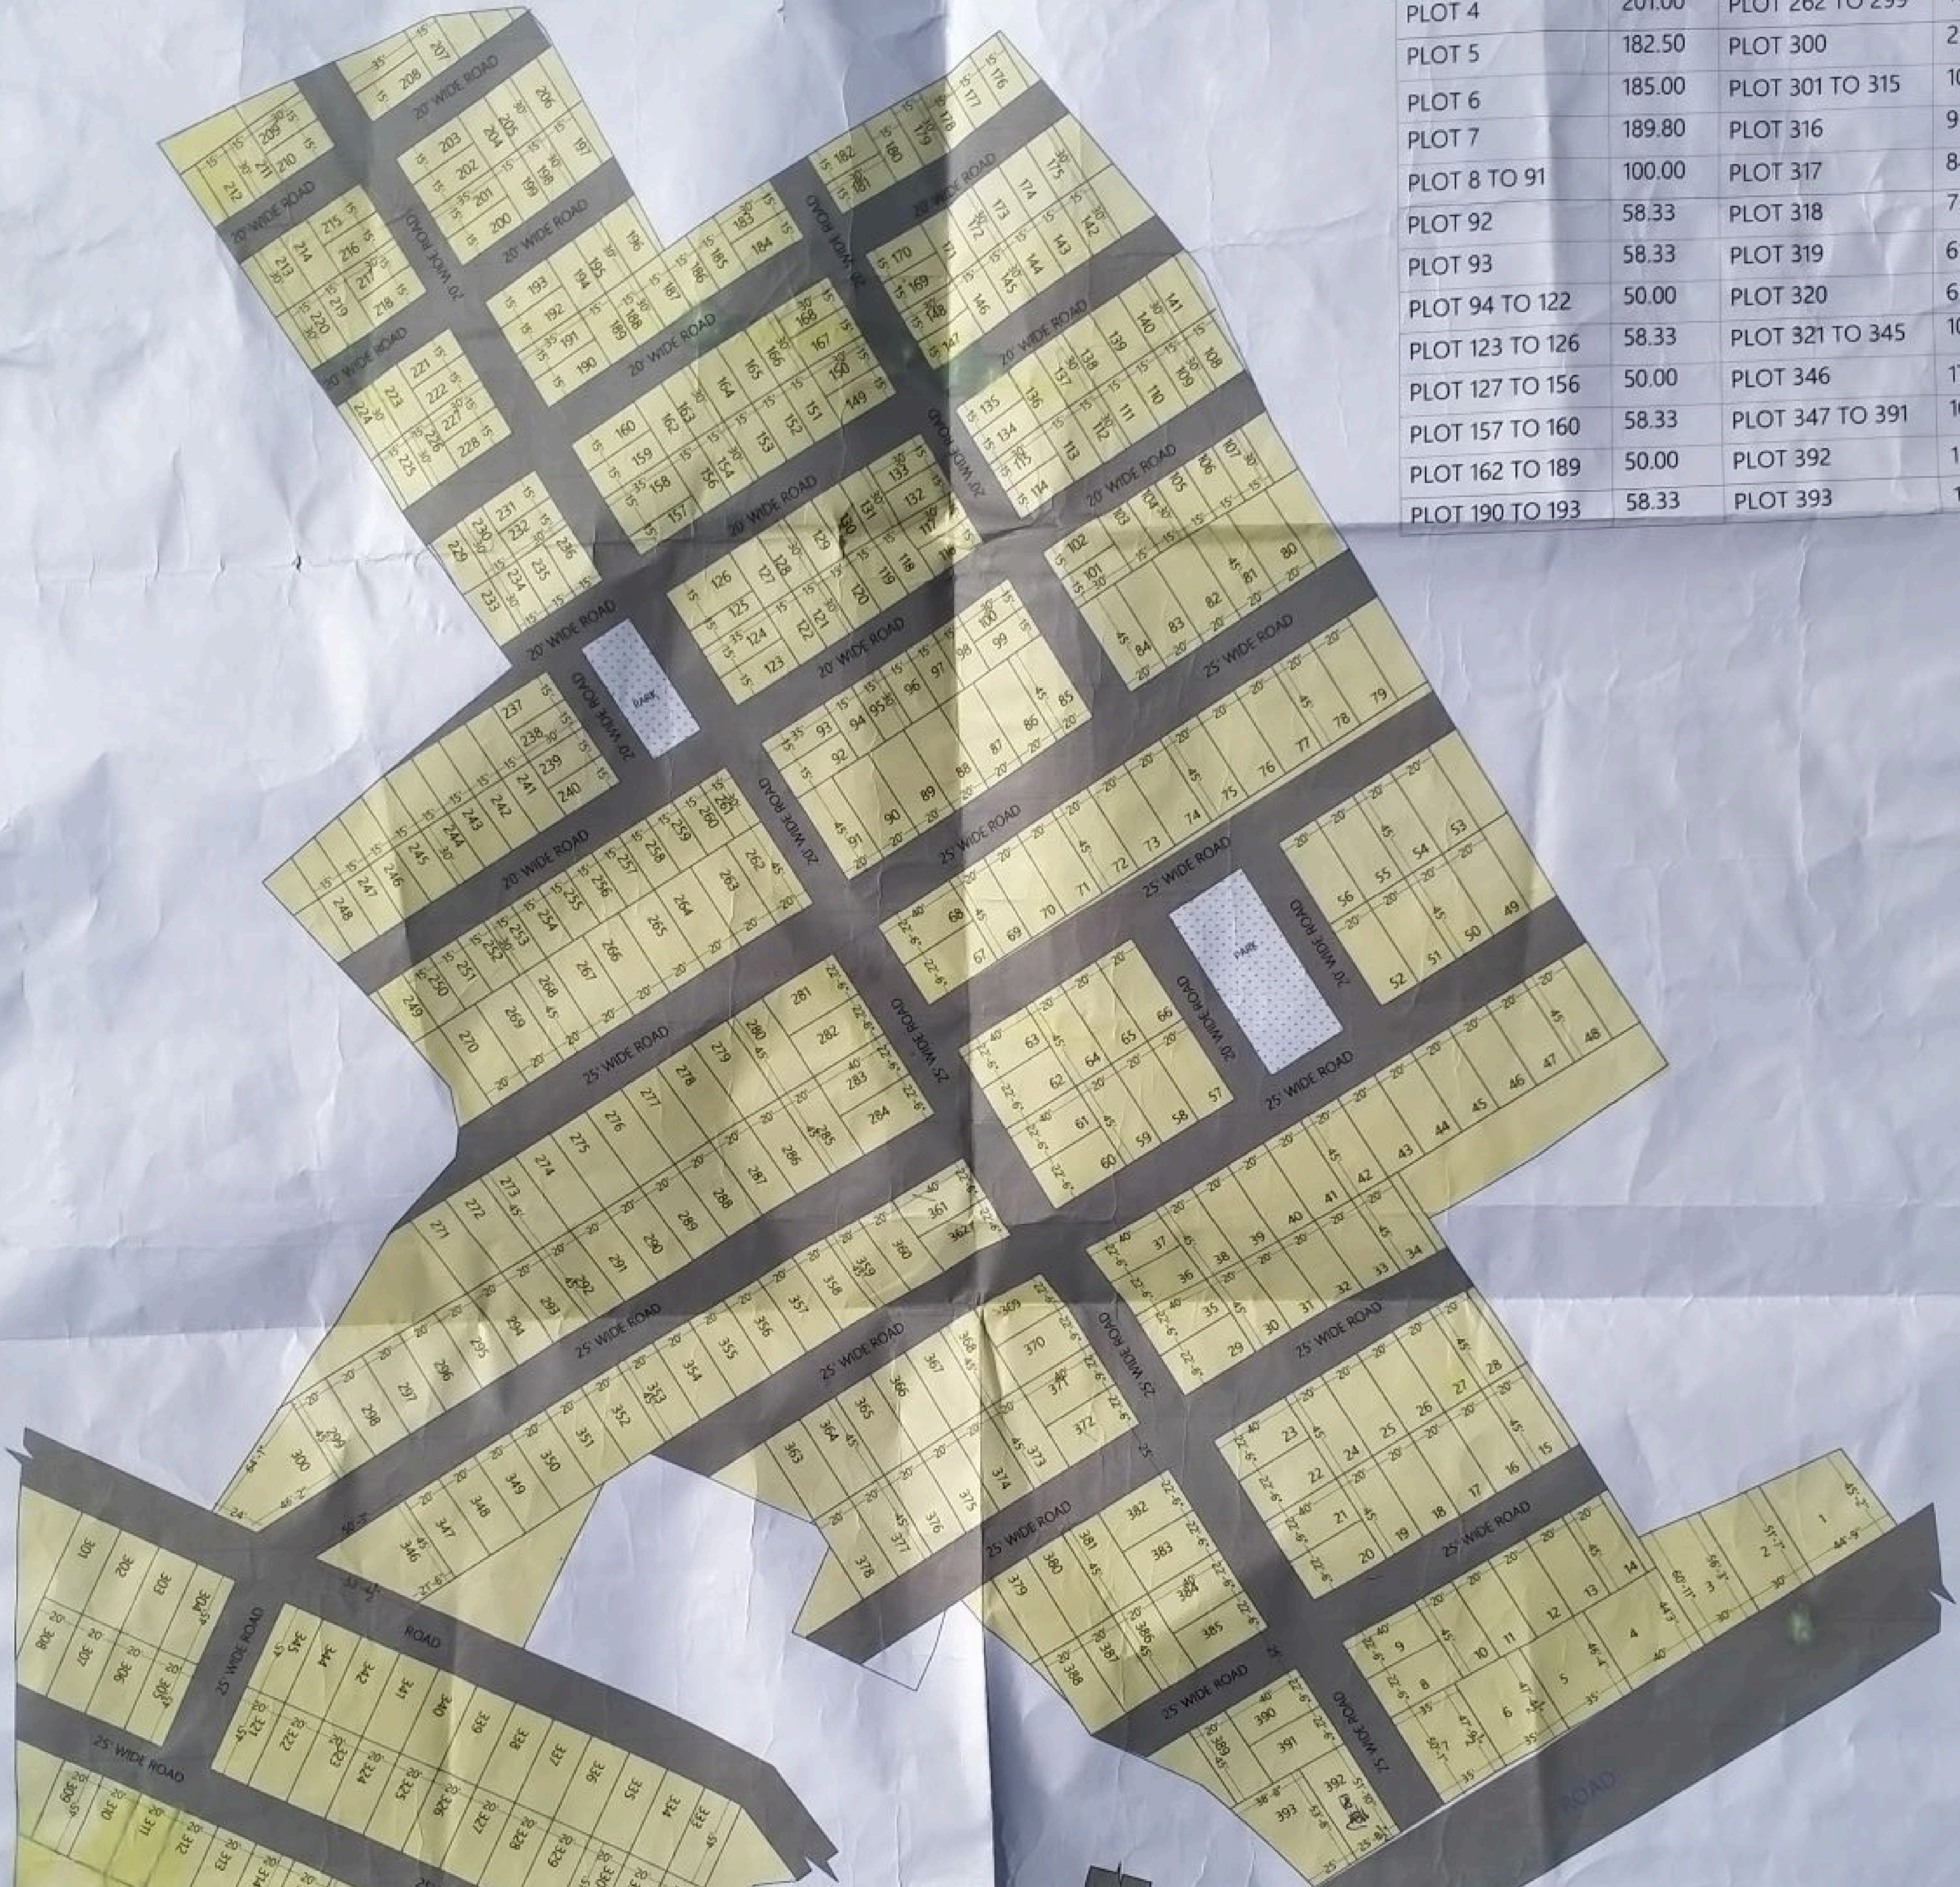

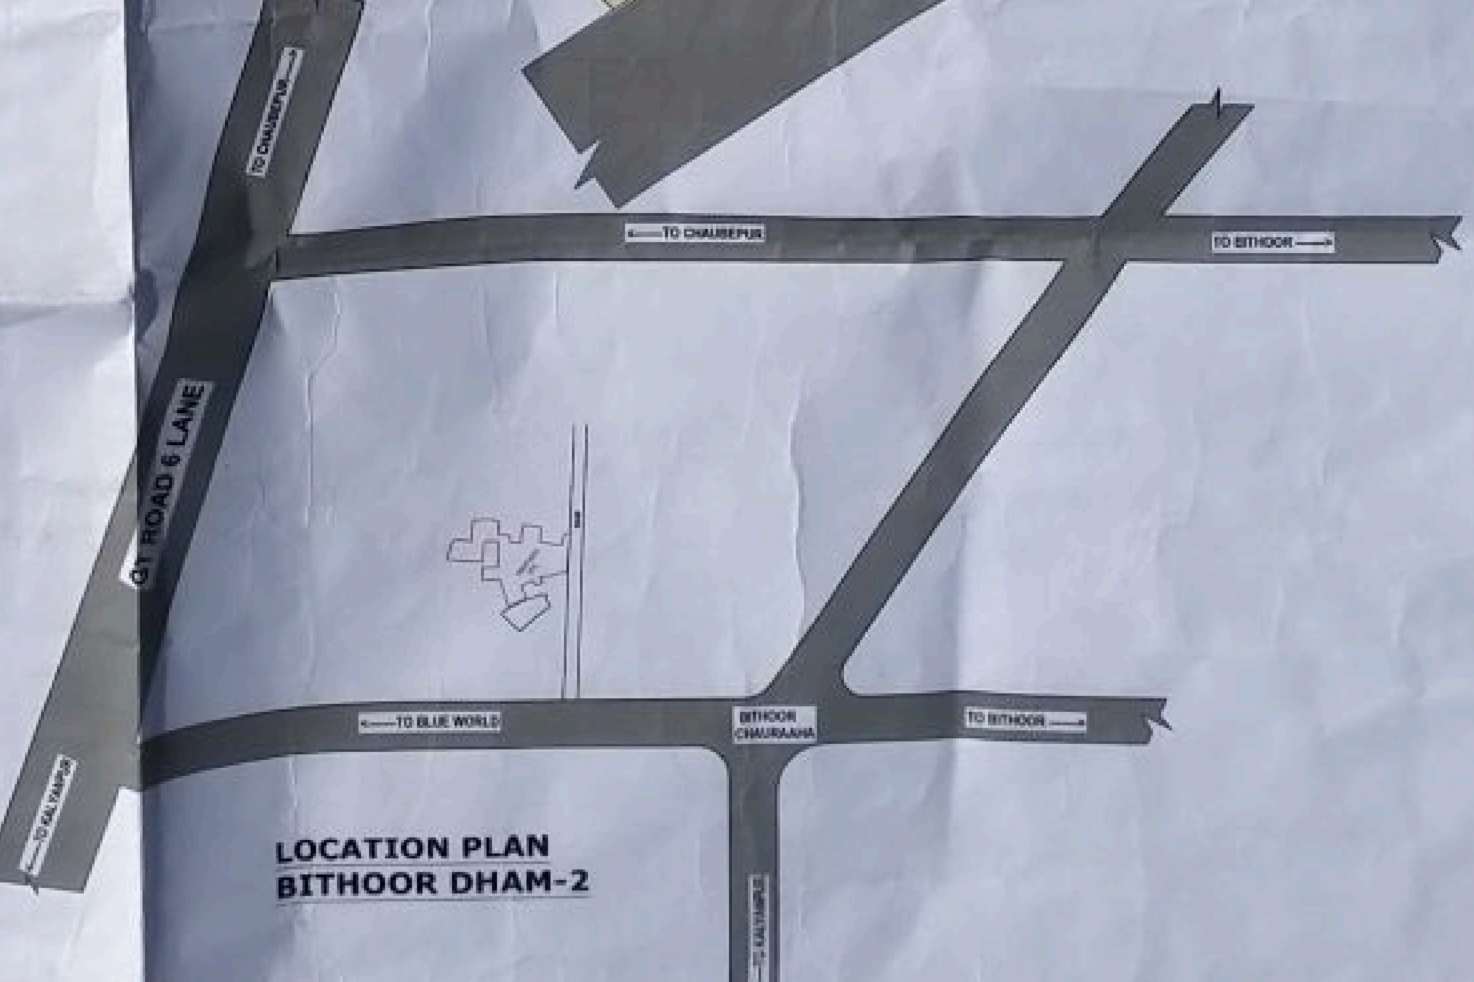

LOCATION PLAN
BITHOOR DHAM-2

Project :

PROPOSED LAYOUT PLAN OF
"JAN SHAKTI BITHOOR DHAM-2"
AT BITHOOR
KANPUR NAGAR

OWNER:

JAN SHAKTI GROUP

Title :

LAYOUT PLAN

North:

Date :

Rev. Date : 05-09-2022

Scale :

Architects :

ARCHITECT & INTERIOR DESIGENERS
117Q/141 SHARDA NAGAR KANPUR.
MO. NO.- 8052377978